




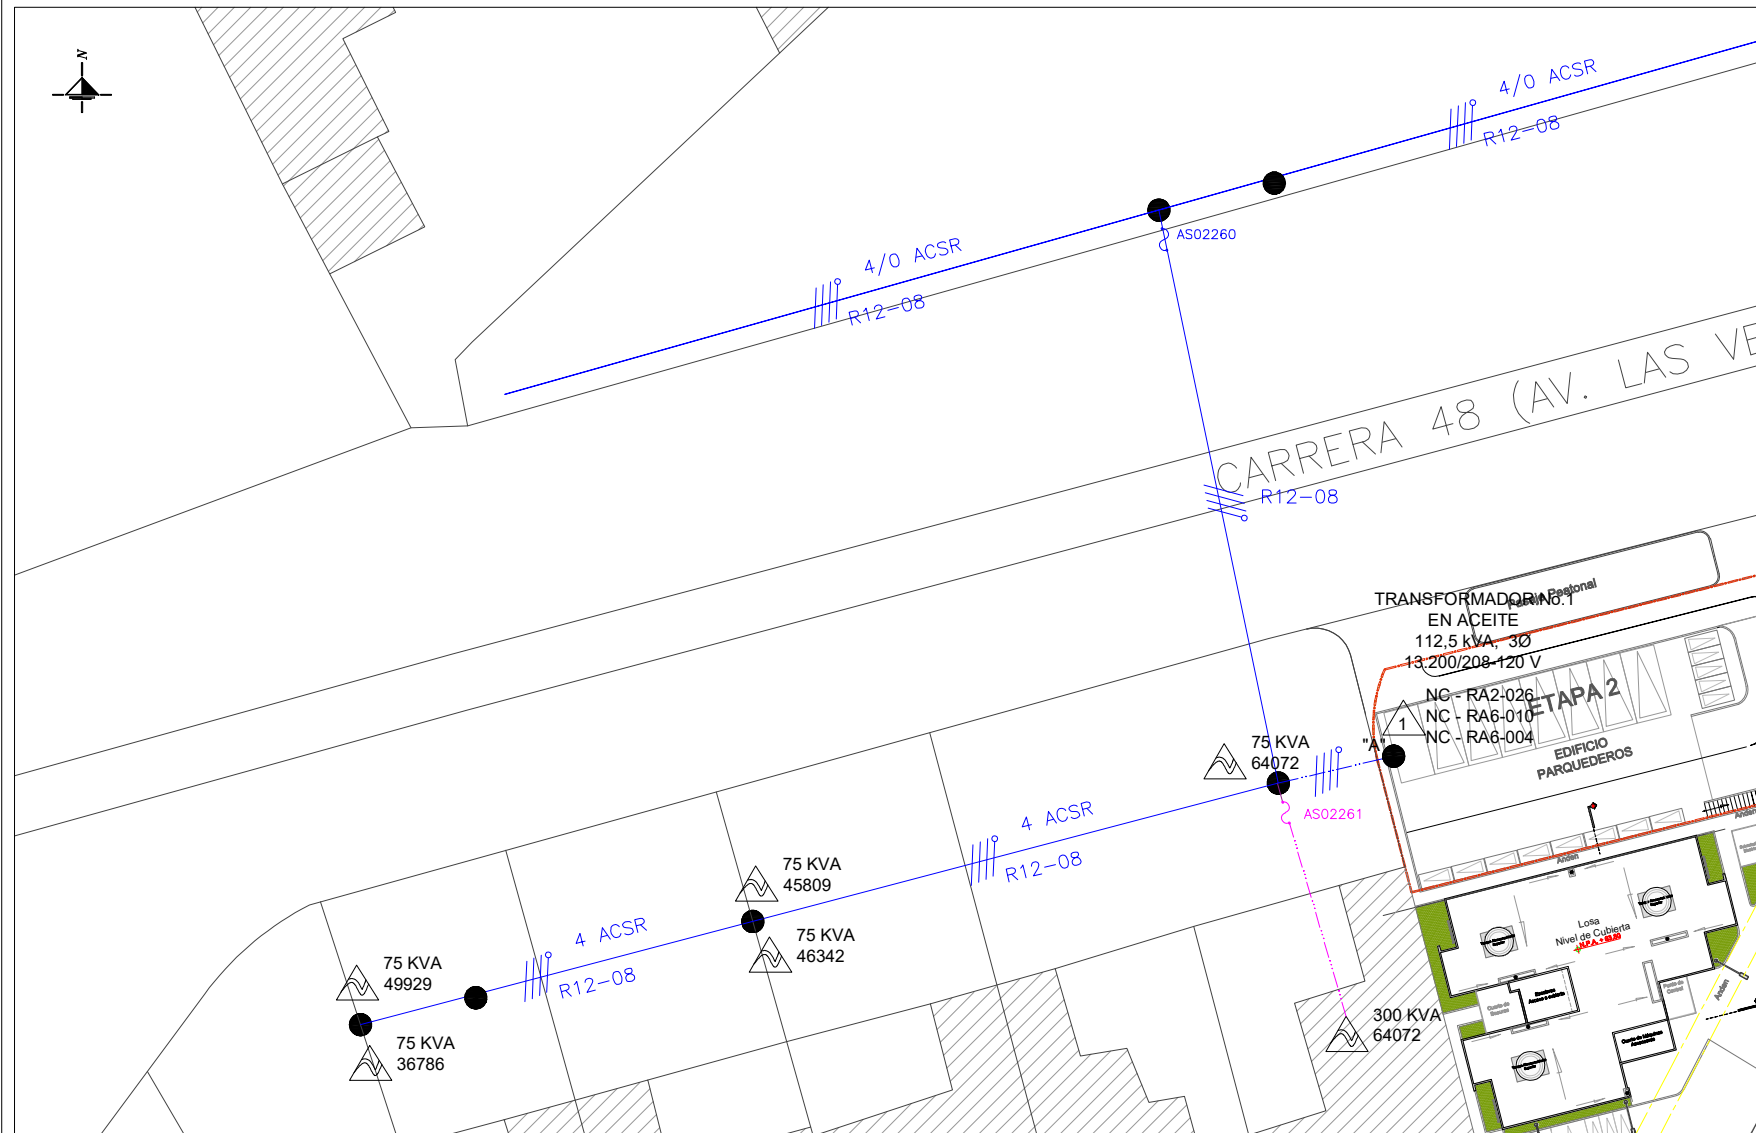

LOCALIZACIÓN Y REDES EN MEDIA TENSION
ESCALA 1:300

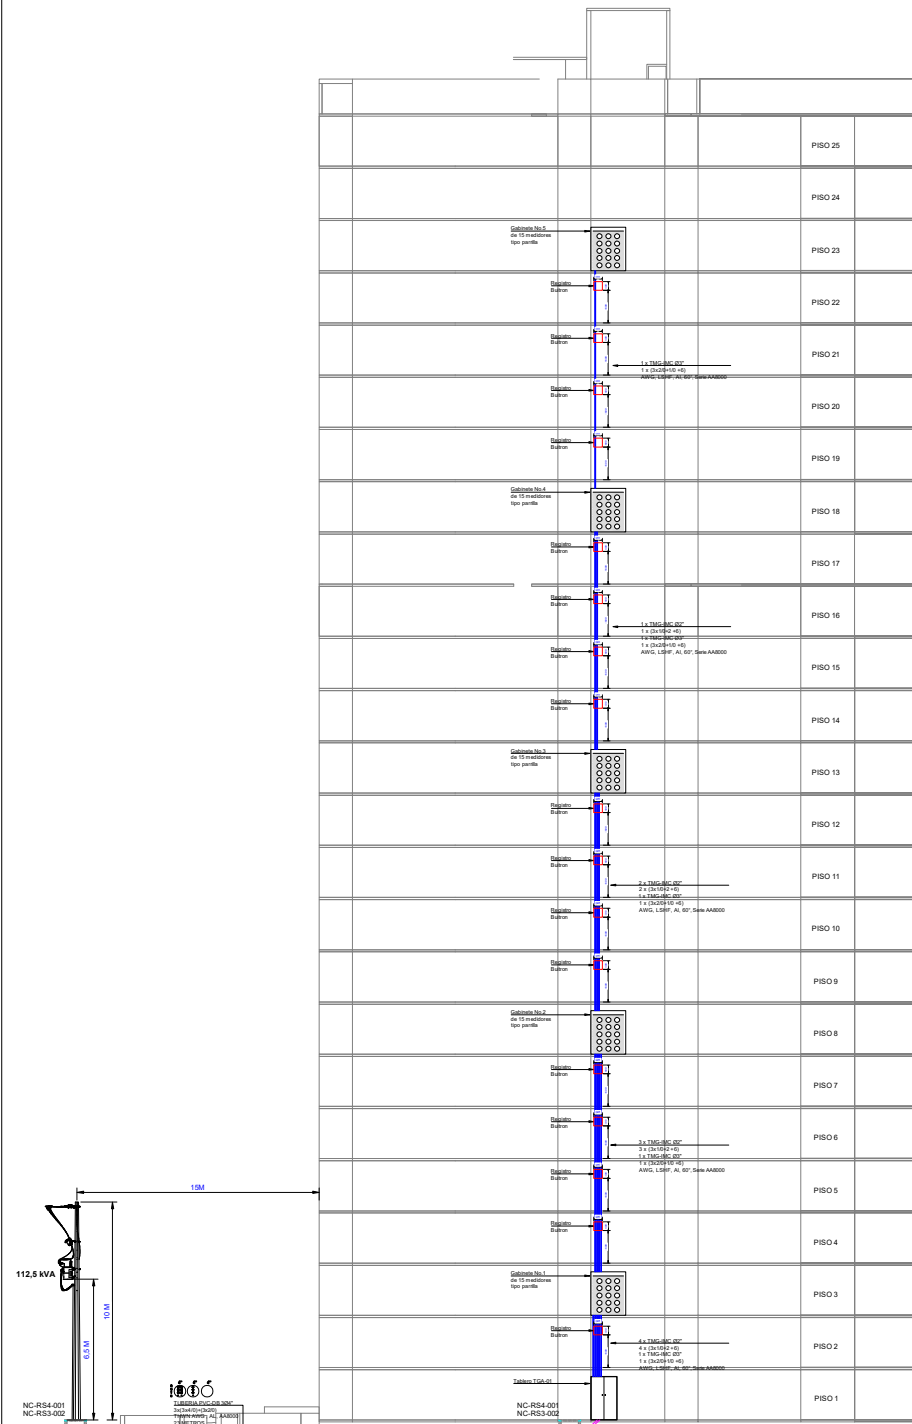

VISTA EN ELEVACION
ESCALA 1:125

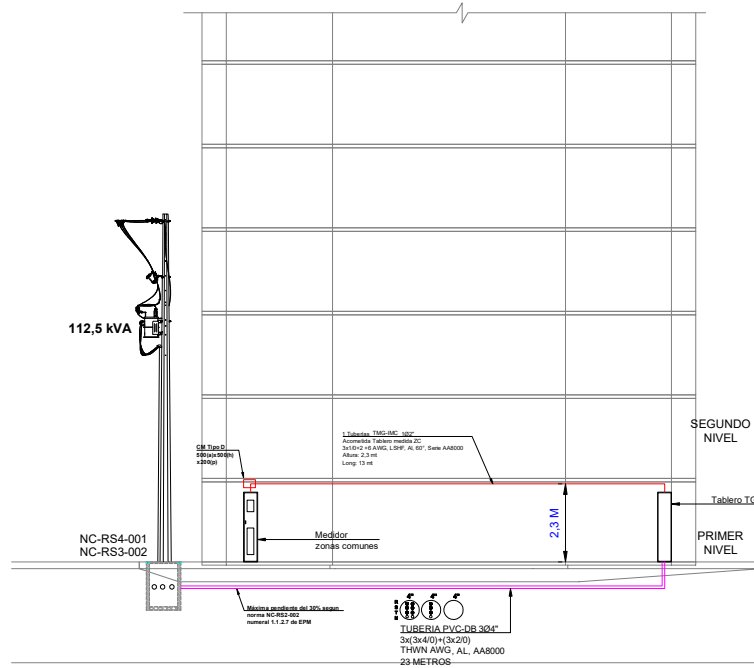

DISTANCIA DE SEGURIDAD (VISTA FRONTAL)
ESCALA 1:125



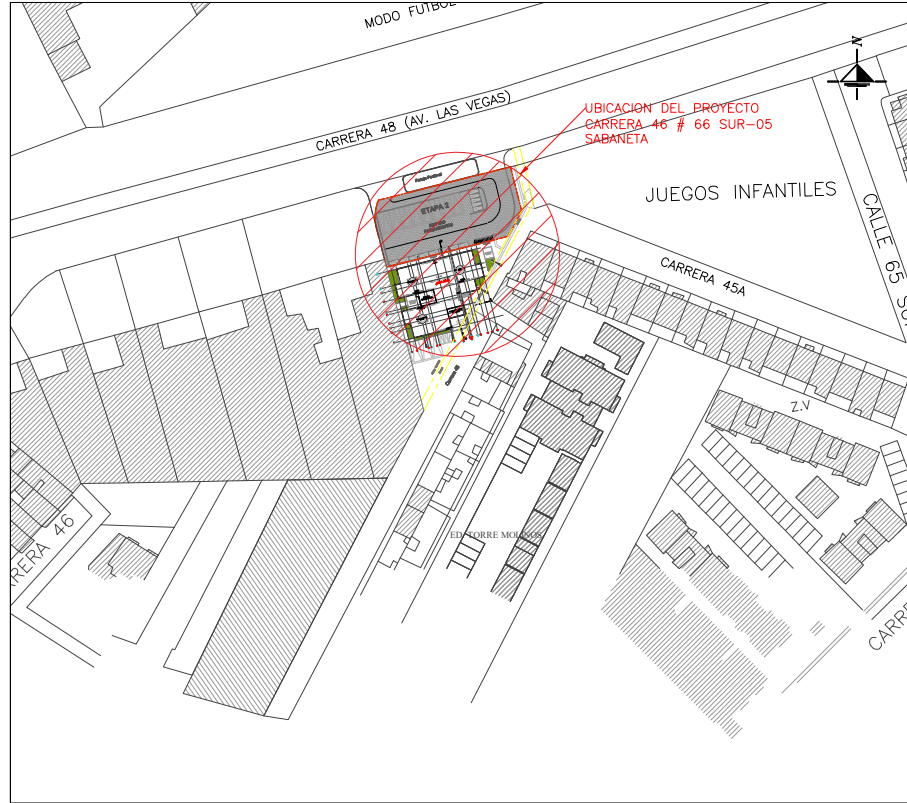



DIAGRAMA DE UBICACION GENERAL
ESCALA 1:1000

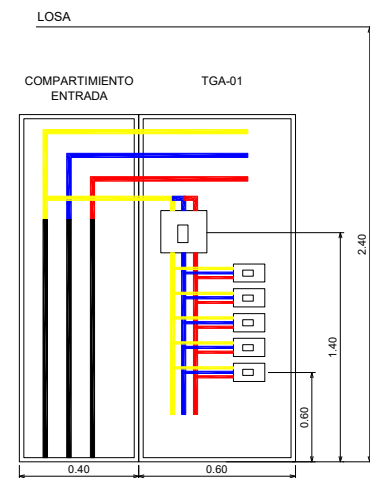


VISTA FRONTAL DE GABINETES
ESCALA SIN

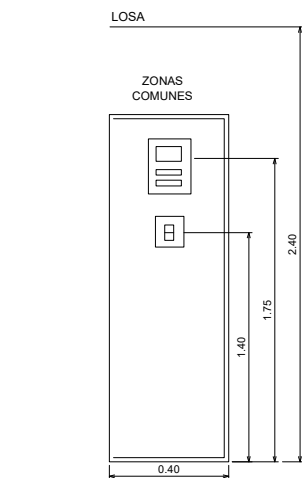


VISTA FRONTAL DE GABINETES
DE MEDIDOR DE ZONAS COMUNES
ESCALA SIN

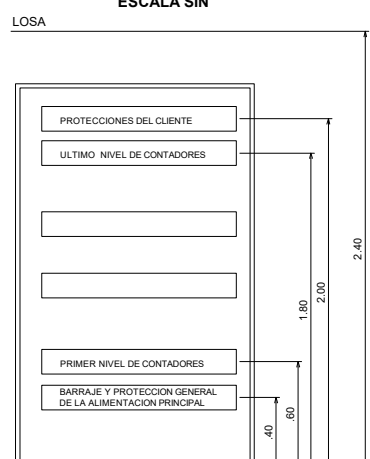

VISTA FRONTAL DE GABINETES
DE MEDIDORES PISOS 3, 8, 13, 18, 23
ESCALA SIN

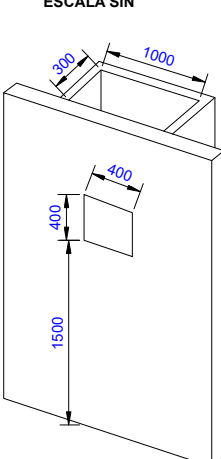

VENTANA DE
INSPECCION
ESCALA SIN

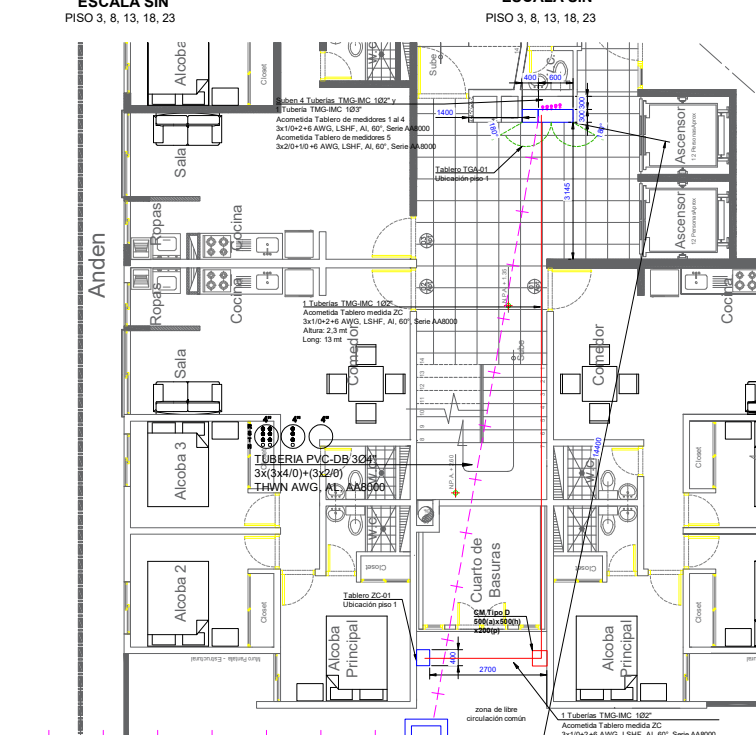

REDES EN BAJA TENSION
ESCALA 1:100


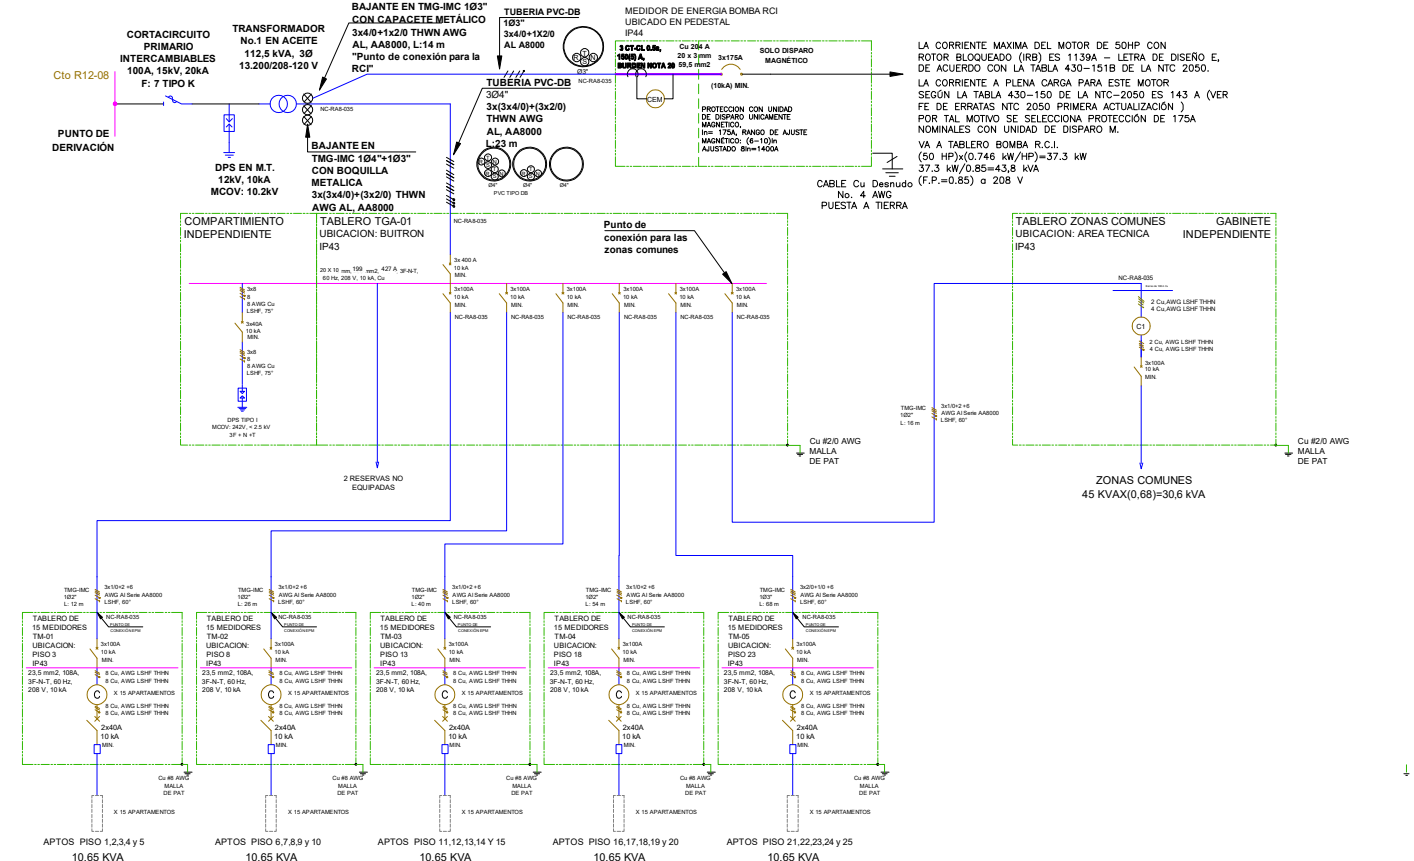


DIAGRAMA UNIFILAR GENERAL
ESCALA 1:1


CUADRO DE CARGAS ESTRATO 3 USO RESIDENCIAL

No TRAFIO	kVA/ TRAFIO	No INSTALACIONES	kVA/ INST	F.D	kVA TOTAL	% CARGA	% REGULACION
1	112.5	75 APARTAMENTOS ESTRATO 3	0,71	1	53,25		0,9
		ZONAS COMUNES	30,6	1	30,6	113,5%	
		BOMBA RCI 50 HP	43,8	1	43,8		0,6

DESCRIPCION	EXISTENTE	PROYECTADO
CONTADOR ELECTRONICO DE MEDIDA DIRECTA 3F-4H (120/208V, 10/100A) CLASE 1, ACTIVA, REACTIVA CLASE 2 MULTIENERGIA		C1
CONTADOR ELECTRONICO DE MEDIDA DIRECTA 2F-3H TIPO PARRILLA (208/120V, 500A) CLASE 1, ENERGIA ACTIVA		C
CONTADOR ELECTRONICO MULTIENERGIA ENERGIA ACTIVA CLASE 0.5 S. REACTIVA CLASE 2. 5(10)A, 208/120V, 3F-4H.		CEM
TRANSFORMADOR TRIFASICO		
TRANSFORMADOR MONOFASICO		
CABLE PRIMARIO CUBIERTO		
CABLE PRIMARIO DESNUDA		
ACOMETIDA SUBTERRANEA		
CAJA DE DISTRIBUCION MARCADA Y SELLADA		
POSTE EN CONCRETO		
CORTACIRCUITOS PRIMARIO		
DPS MT		
TRANSFORMADOR		
TABLERO		
PUERTA A TIERRA		

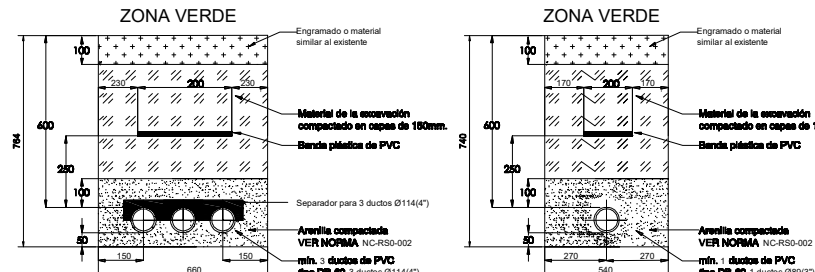

CANALIZACIONES SUBTERRANEAS
VER NORMAS RS0-002, RS1-003, RS1-004

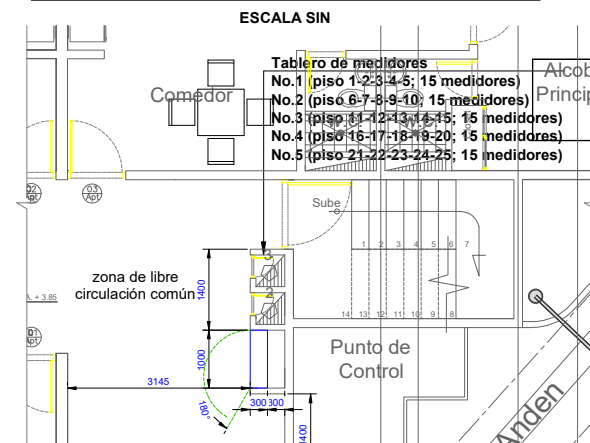

REDES EN BAJA TENSION
ESCALA 1:75

NOTAS

- ESTE PROYECTO CONSISTE EN EL DISEÑO DE UNA SUBESTACION DE 112.5 KVA, PARA ABASTECER 75 APARTAMENTOS Y ZONAS COMUNES Y BOMBA RCI, PARA EL EDIFICIO SAN JOAQUIN UBICADO EN LA CR 46 # 66 SUR - 5 CIUDAD DE SABANETA, ANTIOQUIA.
- LA RED PRIMARIA AEREA EXISTENTE ES PROPIEDAD DE EPM CON NIT 89004966-1.
- SI AL MOMENTO DEL RECIBO TECNICO DEL PROYECTO SE REQUIERAN PERMISOS POR PARTE DE TERCEROS, ESTOS SERAN TRAMITADOS POR EL INTERESADO Y DEBEN SER ANEXADOS AL PROYECTO.
- LOS REDES DE ENERGIA ANTES DE MEDIDA DEBERAN CRUZAR POR ZONAS DE LIBRE CIRCULACION Y COMUNES, EN NINGUN CASO POR EL SUBSUELO O ADOSSADAS A LOSAS DE ZONAS PRIVADAS.
- TODO TUBO EXPUESTO, O QUE ESTE DETRAS DE CIELO FALSO Y/O BUITRONES ANTES DE EQUIPOS DE MEDIDA, SERA METALICO GALVANIZADO, TIPO PESADO.
- ESTE PROYECTO SE REVISARA HASTA LAS PROTECCIONES UBICADAS INMEDIATAMENTE DESPUES DE LOS EQUIPOS DE MEDIDA.
- NORMAS COMPLEMENTARIAS:
NC-RS0-012, NC-RS0-014, NC-RS0-030, NC-RS0-039, NC-RS0-040, NC-RS0-002, NC-RS1-001, NC-RS1-003, NC-RS4-001.
SI AL EJECUTAR LA CONSTRUCCION SE REQUIERE ALGUNA NORMA ADICIONAL VIGENTE AL MOMENTO DEL VISTO BUENO DE ESTE DISEÑO, EL CUMPLIMIENTO DE ESTA SERA REQUISITO PARA LEGALIZAR EL SERVICIO.
- LA REVISION DE ESTE PROYECTO POR PARTE DE EPM NO GARANTIZA SU CUMPLIMIENTO CON EL RETIE, EL DISEÑADOR Y EL CONSTRUCTOR DEBERAN VERIFICARLO.
- SE ANEXA LICENCIA DE CONSTRUCCION SEGUN RESOLUCION No.20237723 DEL 03 DE AGOSTO DE 2023 DEL MUNICIPIO DE SABANETA.
- PUNTO DE CONEXION OTORGADO MEDIANTE SOLICITUD NO. PED-3465676-F7W0.
- EL TRANSFORMADOR Y LAS REDES DE USO GENERAL, PROYECTADAS HASTA EL PUNTO DE CONEXION ASIGNADO AL PROYECTO, SERAN PROPIEDAD DE EPM, MEDIANTE LA FIGURA DE COMPRA DE BIEN FUTURO.
- EL CONSUMO DE ENERGIA DEL ALUMBRADO INTERNO DEBERA QUEDAR REGISTRADO EN EL MEDIDOR DE SERVICIOS COMUNES.
- COMO REQUISITO PARA LA PRESENTACION DE LA SOLICITUD DE RECIBO TECNICO DE ESTE PROYECTO SE DEBERA TENER FORMALIZADO EL CONTRATO DE COMPRA DE BIEN FUTURO ANTE UNIDAD TRANSACCIONES T&O ENERGIA.
- SOLO SE PERMITE EL CRUCE DE CANALIZACIONES EN CELDAS DE PARQUEO SIEMPRE Y CUANDO LOS DUCTOS SE INSTALEN EN ZONAS DE LIBRE CIRCULACION COMUN (SUBSUELOS O LA FRANJA DEL TECHO POR DONDE CRUCEN LOS DUCTOS SIEMPRE QUE SE REGISTRE LEGALMENTE COMO ZONA COMUN). EN NINGUN CASO SE PERMITE LA INSTALACION DE CAJAS DE INSPECCION DENTRO DE LAS CELDAS DE PARQUEADORES (PISO O TECHO).
- EPM HA DEFINIDO BASADO EN LA RESOLUCION CREG 070 DE 1998, QUE LAS REDES DE USO GENERAL, REQUERIDAS PARA CONECTAR EL PROYECTO DEL ASUNTO SERAN DE PROPIEDAD DEL OPERADOR DE RED.
- LOS DUCTOS DE MEDIDA CALIBRADOS POR OTRO LABORATORIO DIFERENTE AL DE EPM DEBE INGRESAR A LAS BASES DE DATOS DEL OPERADOR DE RED ANTES DE SER INSTALADOS. DIRECCION: CARRERA 65 N° 29-18 BARRIO BELÉN TRINDAD.
- EL FACTOR DE DEMANDA SELECCIONADO DEPENDE UNICAMENTE DEL CRITERIO DEL INGENIERO DISEÑADOR BASADO EN EL CONOCIMIENTO DE LAS CARACTERISTICAS PARTICULARES DE ESTE PROYECTO. ESTE Y SUS RESPECTIVAS CONSECUENCIAS DEBEN SER NOTIFICADAS AL PROPIETARIO Y AL REVISOR CON ANTERIORIDAD. EPM NO SE HACE RESPONSABLE POR LA SELECCION DE ESTE FACTOR.
- EPM REALIZARA VISITA DE RECIBO TECNICO, INCLUYE VERIFICACION DE CODIGO DE MEDIDA, REQUISITO PREVIO PARA LA LEGALIZACION DEL SERVICIO. ESTA SE ENCUENTRA DEFINIDA EN LA REGULACION VIGENTE (RESOLUCION CREG 075 DE 2021 Y CIRC 001 DE 2023).
- AL INICIO Y DURANTE LA EJECUCION DE ESTE PROYECTO, ES NECESARIO SOLICITAR CITAS DE RECIBO TECNICO A EPM COMO SE INDICA EN LA NORMA NC-RS0-017.
- PARA DAR CUMPLIMIENTO AL CODIGO DE MEDIDA, AL MOMENTO DEL RECIBO TECNICO DE LA INSTALACION POR PARTE DE EPM, EL INGENIERO RESPONSABLE DEBE PRESENTAR UN INFORME CON EL CALCULO DEL BURDEN REAL Y EL ERROR PORCENTUAL TOTAL DEL VOLTAJE (SE APLICA DE LOS EQUIPOS DE MEDIDA).
- EL DISEÑADOR Y CONSTRUCTOR DE ESTE PROYECTO DE REDES SON RESPONSABLES DE VALIDAR LA NECESIDAD QUE EL AISLAMIENTO Y/O CHABOTRA DE LOS CONDUCTORES ELECTRICOS A UTILIZAR REQUERIRAN POSEER CARACTERISTICAS DE BAJA EMISION DE HUMOS, RETARDANTE A LA LLAMA O RESISTENTE AL FUEGO Y LIBRE O CERO HALOGENOS ACORDE CON LO DISPUESTO EN EL RETIE, ADENAS DE LO ESTIPULADO EN EL CODIGO SISMO RESISTENTE (NSR10) Y LA REGlamentACION DE LA DIRECCION NACIONAL DE BOMBEROS DE COLOMBIA EL INSPECTOR RETIE QUE CERTIFIQUE LA INSTALACION DEBERA VERIFICAR SI SE CUMPLE LO ANTES MENCIONADO.
- LOS CONDUCTORES DE ALUMINIO EN BAJA TENSION DEBERAN SER DE LA SERIE AA8000 COMO LO SOLICITA EL RETIE.
- LOS BUES SECUNDARIOS DEL TRANSFORMADOR DEBERAN SER EN FORMA DE PALA CON PERFORACIONES, PARA LA ADECUADA CONEXION DE VARIOS CONDUCTORES POR FASE.

ESPACIO PARA SELLOS

ESTE PROYECTO REQUIERE DE CERTIFICACION

PLENA DE ACUERDO CON EL RETIE

AREA CONEXION Y VINCULACION

epm REVISADO

Revisó: Cristian Camilo Badajés A

Vo. Bo.

Fecha: Día 27 Mes 10 Año 2023

NOTA: CADUCIDAD DOS (2) AÑO ANTES DE LA EJECUCION DE ESTE PROYECTO DEBE SOLICITARSE RECIBO TECNICO

EDIFICIO SAN JOSÉ CR 46 # 66 SUR - 5 SABANETA, ANTIOQUIA	
DISEÑADOR HERNANDEZ MARRIN CC: 70.070.229 Dirección: Carrera 65 N° 29-18 Celular: 311986070 Correo: herney.hernandez@gmail.com Medellín - Colombia	
PROPIETARIO CONCELESTRA Y MAQUINARIA LTDA NIT: 800.180.763 Dirección: Calle 11 # 3 - 64 Teléfono: 31970441 Correo: general@concelestroymaquinaria.com Calle - Colombia	
CONSEGUIMIENTO DE IDENTIFICACION PROYECTO NO. 23523178	FIRMA HERNANDEZ MARRIN MATECULA AN205 96797
CONTIENE DISEÑO DISEÑADOR DISEÑO DISEÑADOR DISEÑO DISEÑADOR	FECHA NOVIEMBRE DE 2023
ESCALA 1:200	ESCALA 1:200